☐ Aucun choix des couleurs n'est attribué à la vue

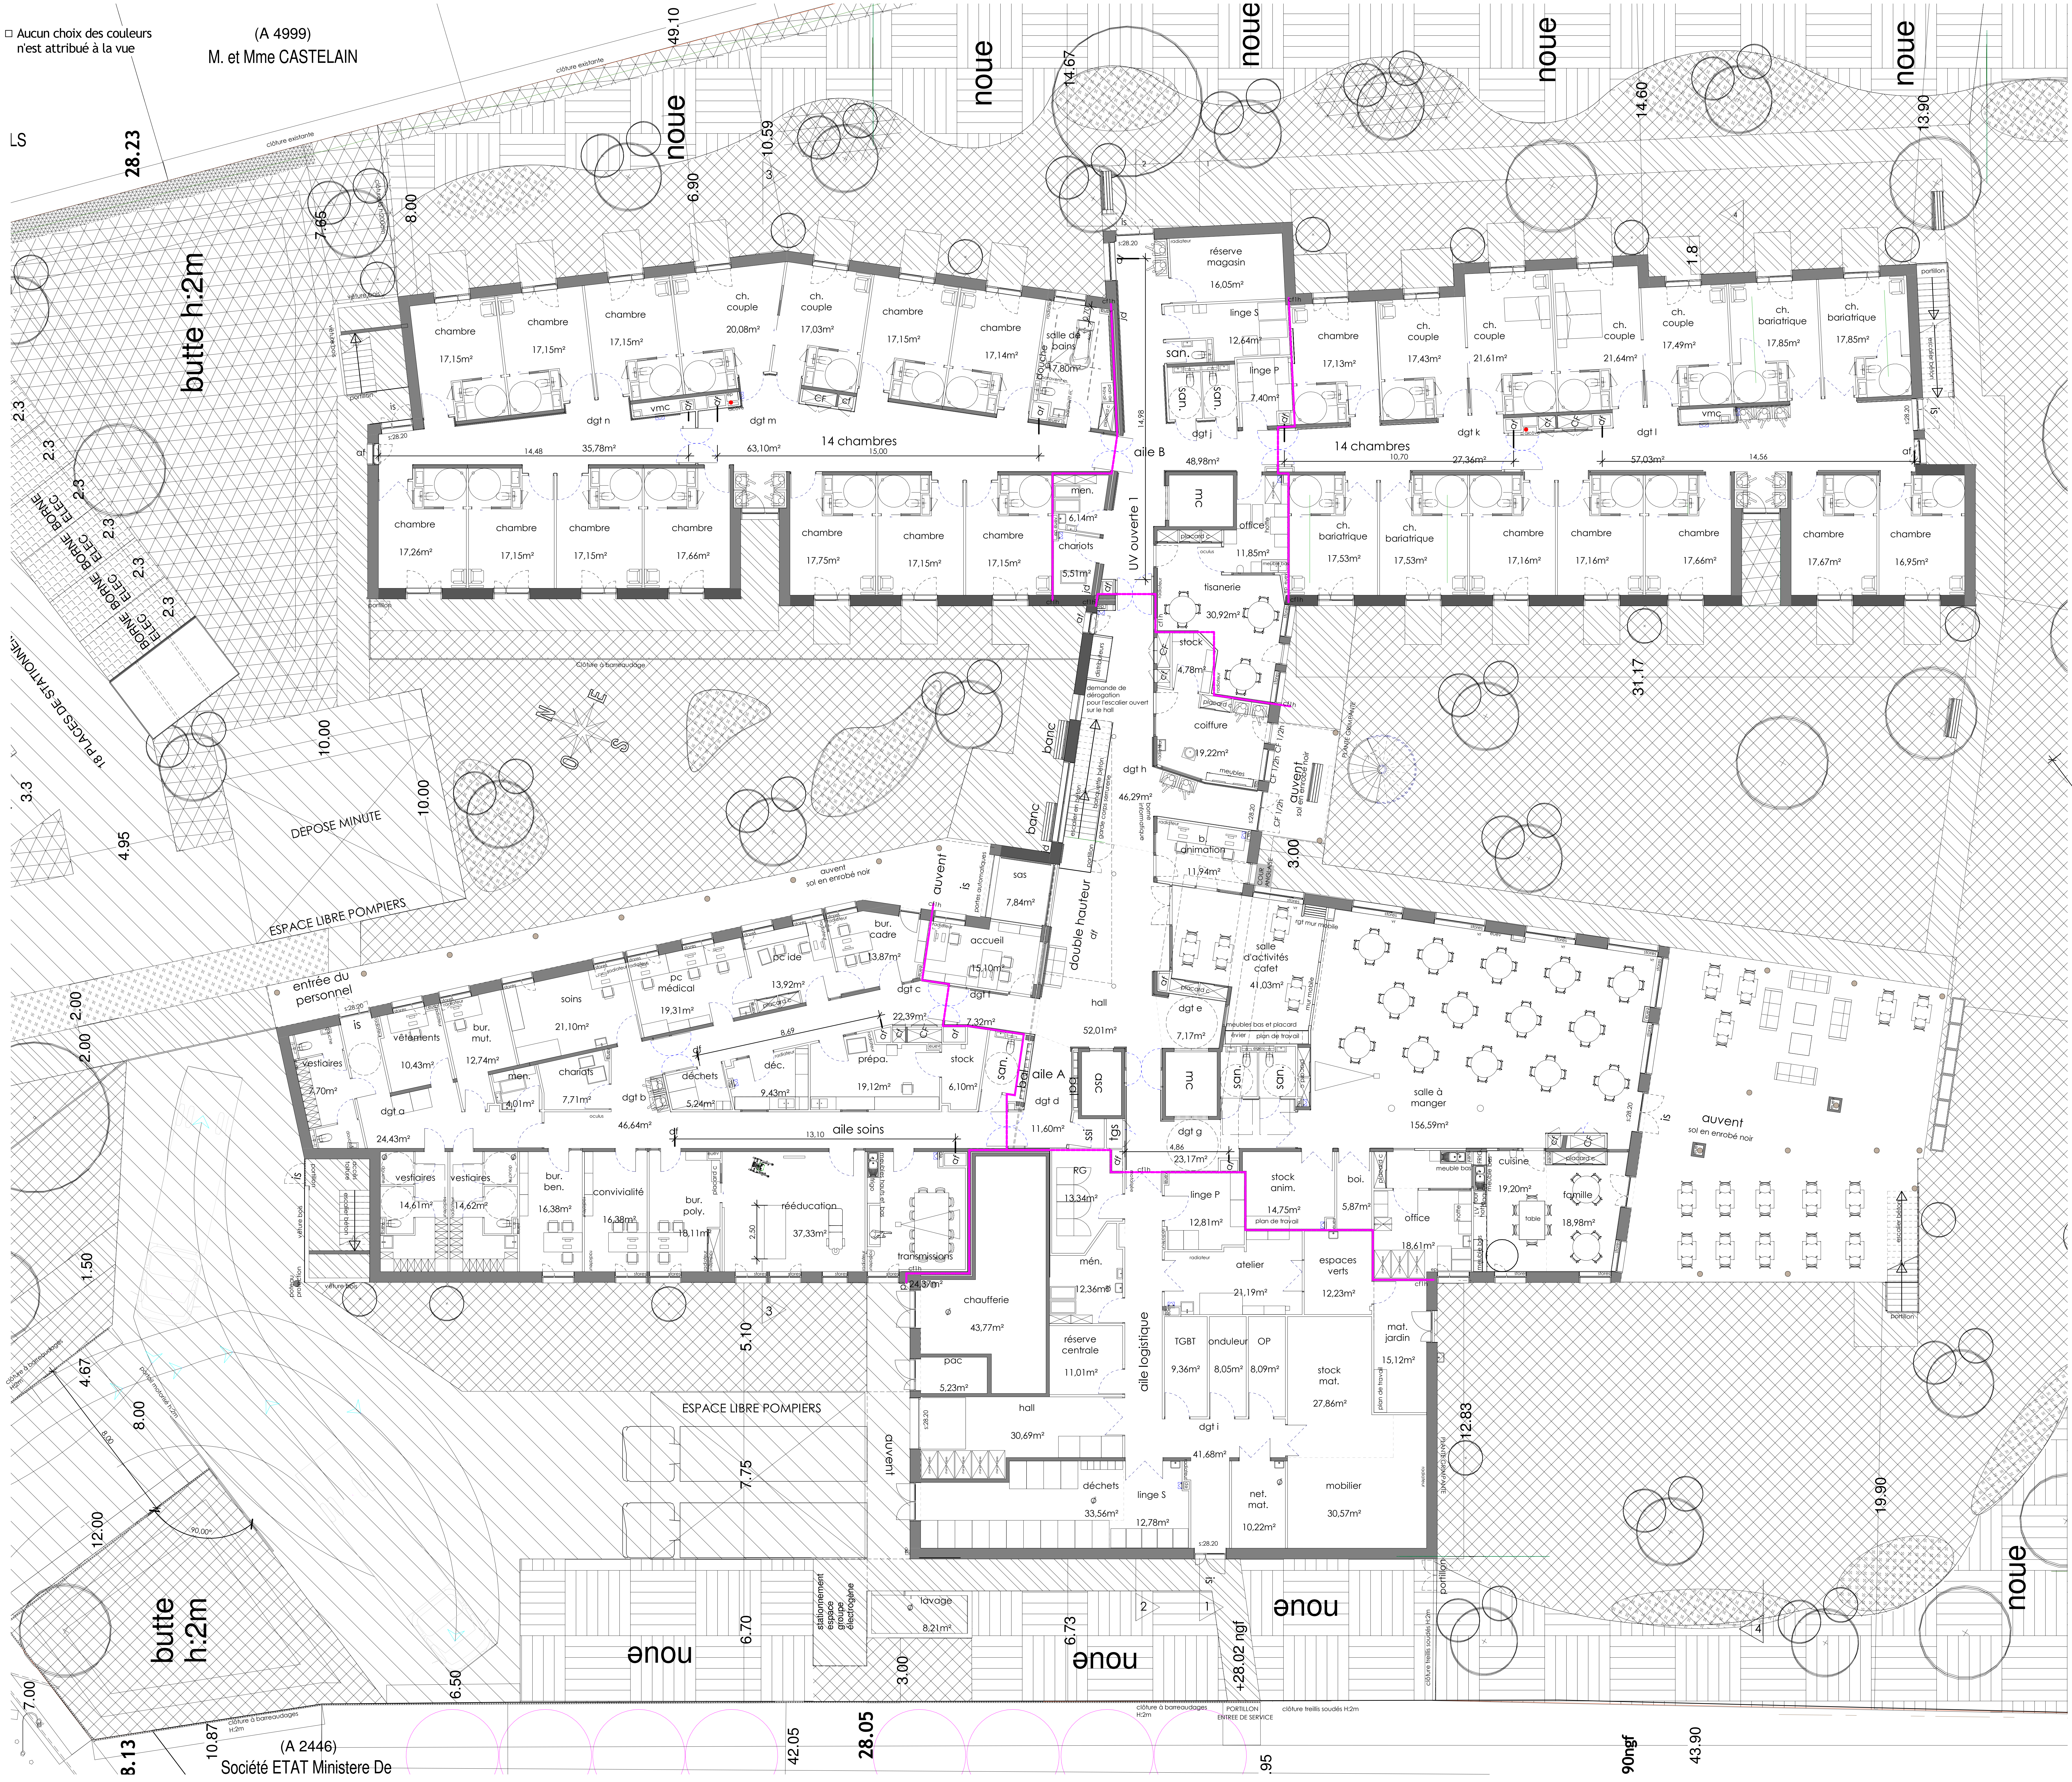
(A 4999)
M. et Mme CASTELAIN
LS
28.23
49.10
clôture existante
noue
noue
noue
noue
noue
noue
noue
noue
noue
butte h:2m
butte h:2m
BORNE ELEC
BORNE ELEC
BORNE ELEC
18 PLACES DE STATIONNEMENT
DEPOSE MINUTE
ESPACE LIBRE POMPIERS
ESPACE LIBRE POMPIERS
chambre 17,15m²
chambre 17,15m²
chambre 17,15m²
ch. couple 20,08m²
ch. couple 17,03m²
chambre 17,15m²
chambre 17,14m²
salle de bains 7,80m²
dgt n
dgt m
vmc
CF
14 chambres
35,78m²
63,10m²
chambre 17,26m²
chambre 17,15m²
chambre 17,15m²
chambre 17,66m²
chambre 17,75m²
chambre 17,15m²
chambre 17,15m²
men. 6,14m²
chariots 5,51m²
UV ouverte 1
aile B
48,98m²
réserve magasin 16,05m²
linge S 12,64m²
linge P 7,40m²
san.
dgt j
mc
office 11,85m²
tisanerie 30,92m²
stock 4,78m²
coiffure 19,22m²
dgt h 46,29m²
animation 11,94m²
auvent sol en enrobé noir
chambre 17,13m²
ch. couple 17,43m²
ch. couple 21,61m²
ch. couple 21,64m²
ch. couple 17,49m²
ch. bariatrique 17,85m²
ch. bariatrique 17,85m²
dgt k 27,36m²
dgt l 57,03m²
14 chambres
ch. bariatrique 17,53m²
ch. bariatrique 17,53m²
chambre 17,16m²
chambre 17,16m²
chambre 17,66m²
chambre 17,67m²
chambre 16,95m²
31.17
demande de dérogation pour l'escalier ouvert sur le hall
banc
banc
auvent sol en enrobé noir
auvent
sas 7,84m²
accueil 15,10m²
bur. cadre 13,87m²
pc ide 13,92m²
pc médical 19,31m²
soins 21,10m²
entrée du personnel
vêtements 10,43m²
bur. mut. 12,74m²
vestiaires 7,70m²
men. 4,01m²
chariots 7,71m²
dgt a 24,43m²
dgt b 46,64m²
déchets 5,24m²
déc. 9,43m²
prépa. 19,12m²
stock 6,10m²
dgt c 22,39m²
dgt f 7,32m²
san.
aile A
dgt d 11,60m²
double hauteur
hall 52,01m²
asc
mc
ssi
tgs
dgt e 7,17m²
dgt g 23,17m²
aile soins
vestiaires 14,61m²
vestiaires 14,62m²
bur. ben. 16,38m²
convivialité 16,38m²
bur. poly. 18,11m²
rééducation 37,33m²
transmissions 24,37m²
salle d'activités cafet 41,03m²
salle à manger 156,59m²
auvent sol en enrobé noir
cuisine
famille 18,98m²
office 18,61m²
boi. 5,87m²
stock anim. 14,75m²
linge P 12,81m²
RG 13,34m²
mén. 12,36m²
atelier 21,19m²
espaces verts 12,23m²
chaufferie 43,77m²
pac 5,23m²
réserve centrale 11,01m²
aile logistique
TGBT 9,36m²
onduleur 8,05m²
OP 8,09m²
stock mat. 27,86m²
mat. jardin 15,12m²
hall 30,69m²
dgt i 41,68m²
déchets 33,56m²
linge S 12,78m²
net. mat. 10,22m²
mobilier 30,57m²
auvent
ESPACE LIBRE POMPIERS
lavage 8,21m²
stationnement espace groupe électrogène
+28.02 ngf
PORTILLON ENTREE DE SERVICE
clôture à barreaudages H:2m
clôture treillis soudés H:2m
(A 2446)
Société ETAT Ministere De
28.05
42.05
43.90
90ngf
12.83
19.90
7.75
6.70
6.73
5.10
3.00
12.00
8.00
4.67
1.50
2.00
4.95
3.3
10.00
7.65
8.00
6.90
10.59
14.67
14.60
13.90
1.8

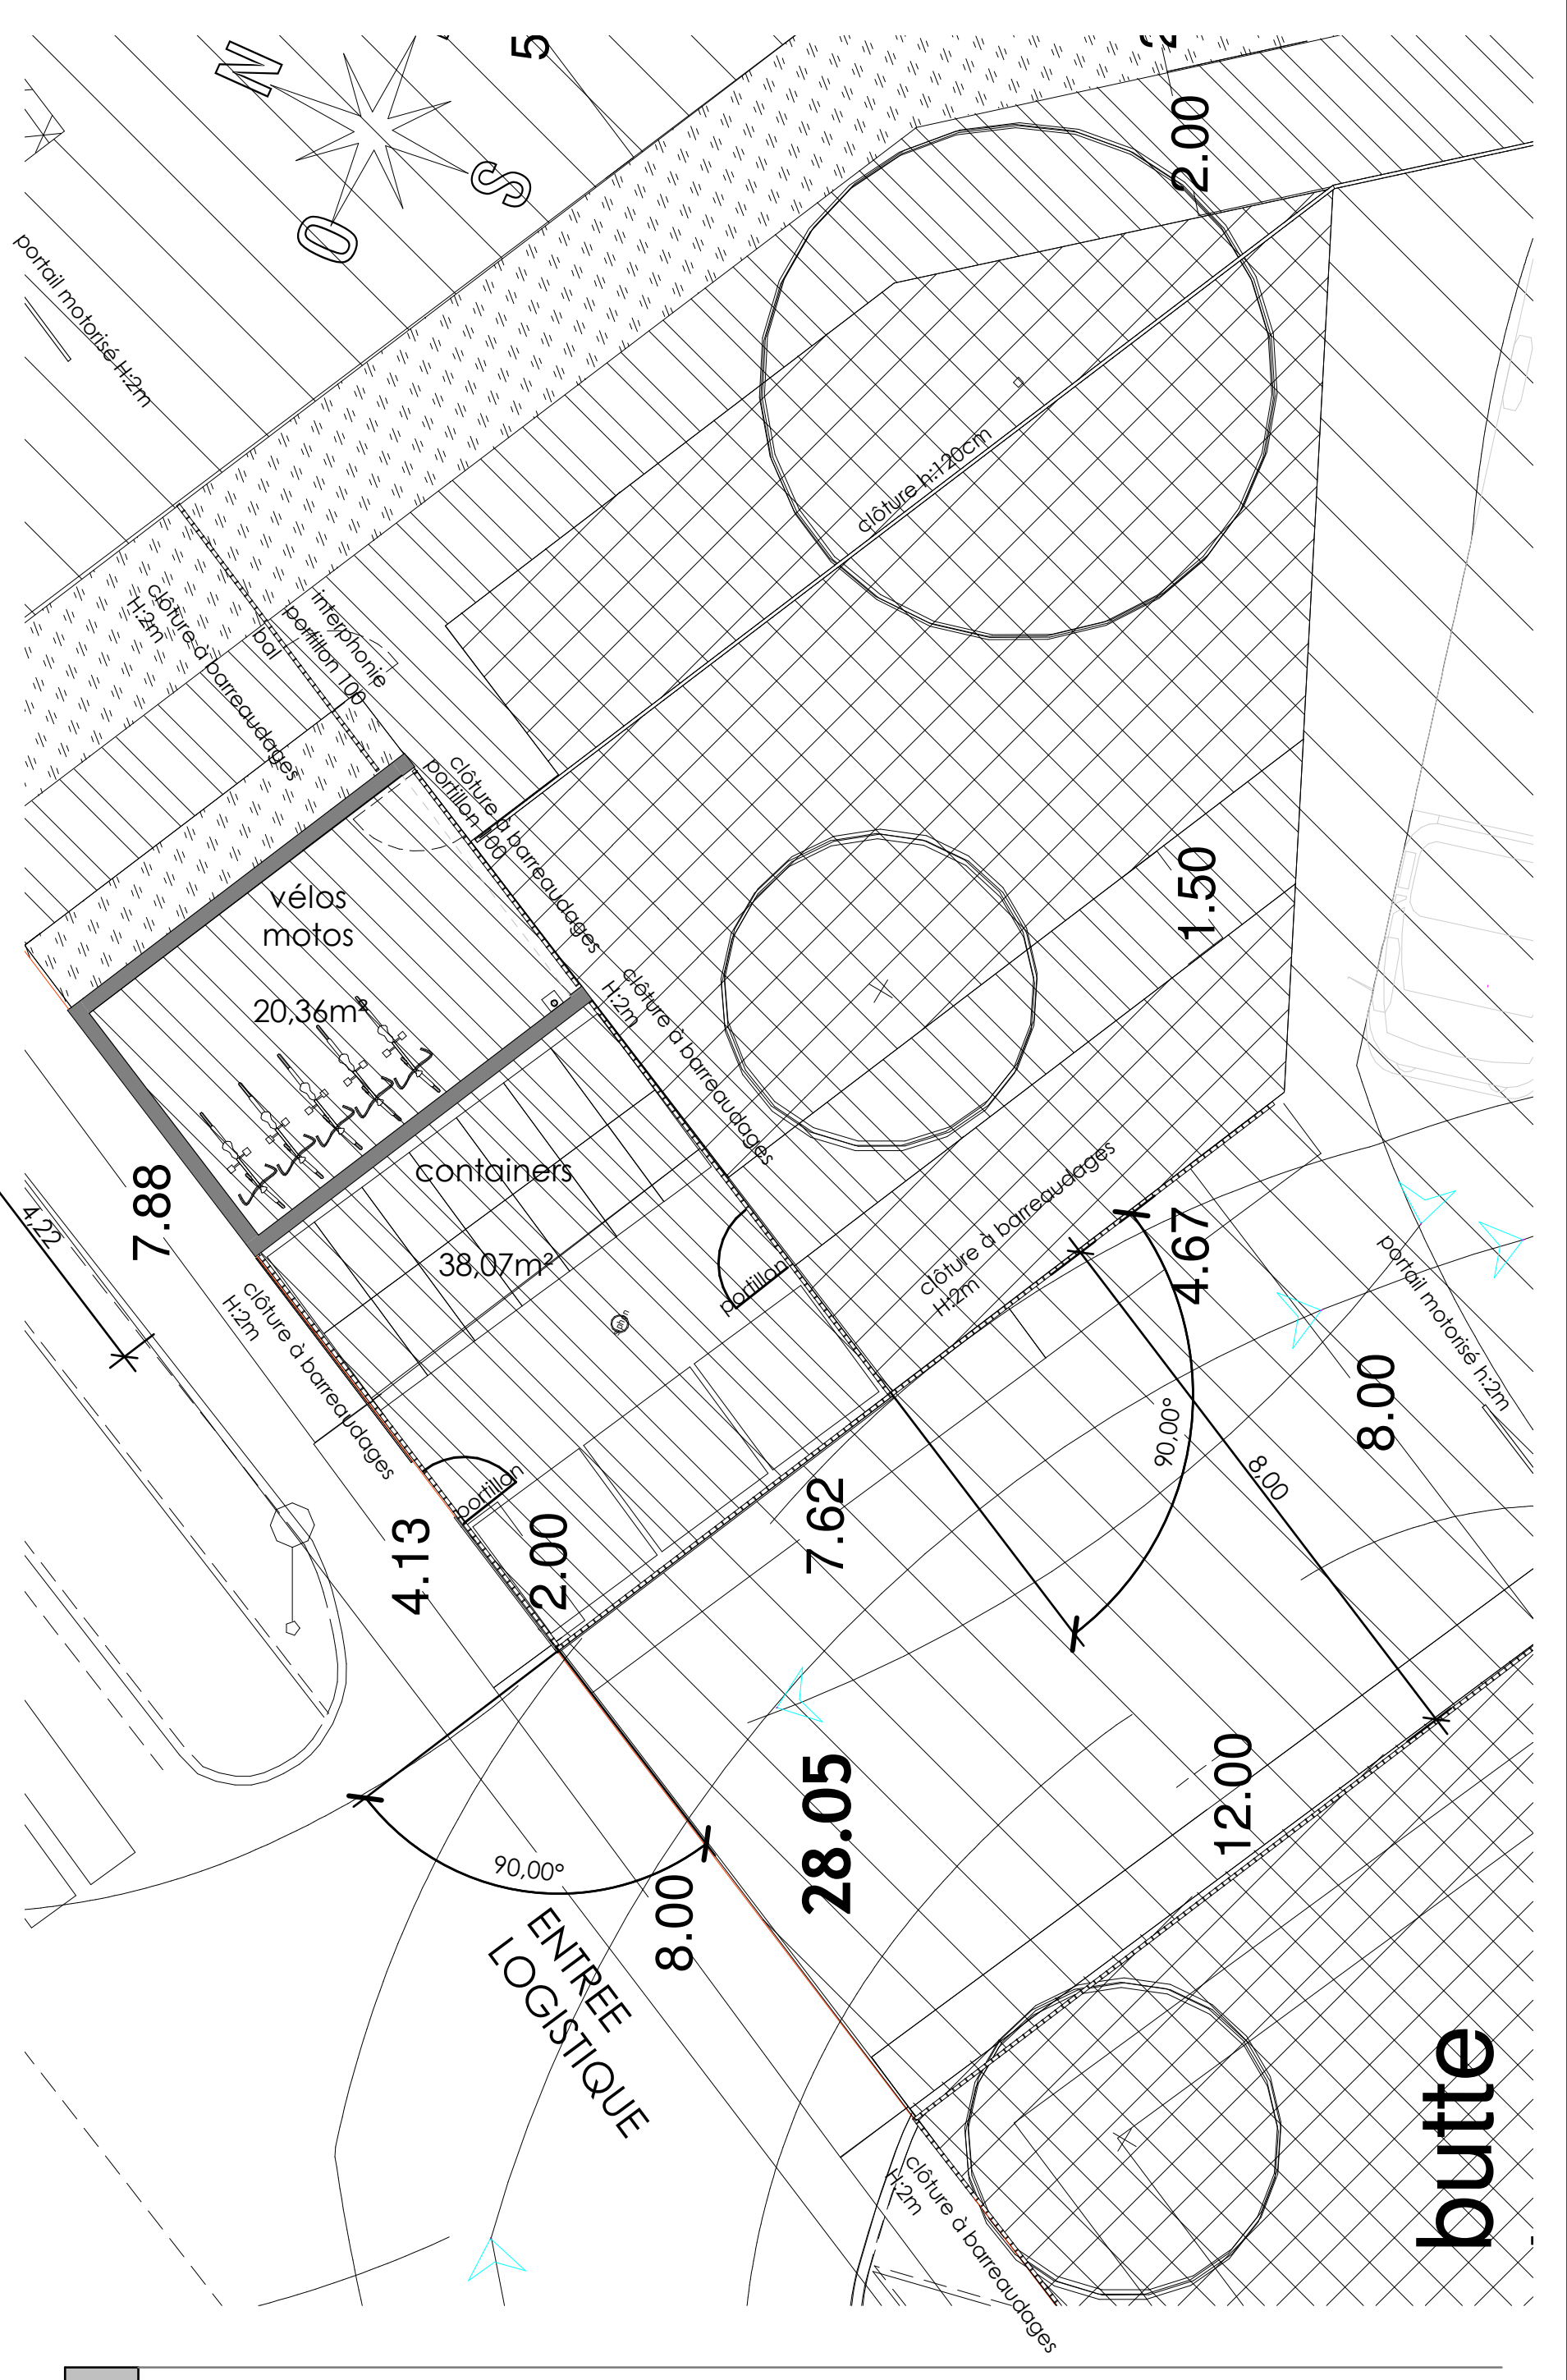
vélos motos 20,36m²
containers 38,07m²
ENTREE LOGISTIQUE
butte
28.05
8.00
12.00
7.88
7.62
4.13
2.00
4.67
1.50
2.00
5
90,00°

2 R+0 100 - ENTREE
Ech : 1 : 100

Affaire n° : **19.05**

Projet : **EHPAD DE 81 LITS**
170 route de Lille, La Bassée

Maître d'ouvrage : GHT de l'Artois
CH LENS BAT A1 99 rte de La Bassée SP8 62307 Lens Cedex
tél : 03 21 69 16 37

AMO : MCI
120, rue Esquermes 59000 Lille
tél : 03 20 05 10 80

AMO : ASCOH
10, zac carrière dorée 59310 Orchies
tél : 07 69 47 80 12

Architectes PAINDAVOINE PARMENTIER
101 rue Louis Constant - 59650 Villeneuve d'Ascq
tél : 03 20 05 22 15

Architectes AVANT PROPOS
51, BVD de Belfort - 59042 Lille cedex
tél : 03 20 62 10 00

Paysagistes KVDS
340, av de la Marne - Parc Europe - Bat 11 - 59700 Marcq en Baroeul
tél : 03 20 89 39 80

BET PROJEX / PROBIM
30, place S. Allende - 59650 - Villeneuve d'Ascq
tél : 03 20 47 03 01

BET EGIS
165, av de la Marne - CS 32005 59702 Marcq-en-Baroeul Cedex
tél : 03 20 28 31 38

BET HQE DIAGOBAT
30, place S. Allende - 59650 - Villeneuve d'Ascq
tél : 03 20 47 23 20

Codification :

PHASE	EMETTEUR	LOT	TYPE	NIVEAU	ZONE	NUMERO	INDICE
DCE	PPA	ARC		N00	TZ	AR01	0

Nom du document : **PLAN DU RDC**
Echelle : 1/100
Modifications :

N°	Description	Date
0	première diffusion	06/22

20/06/2022 14:39:15