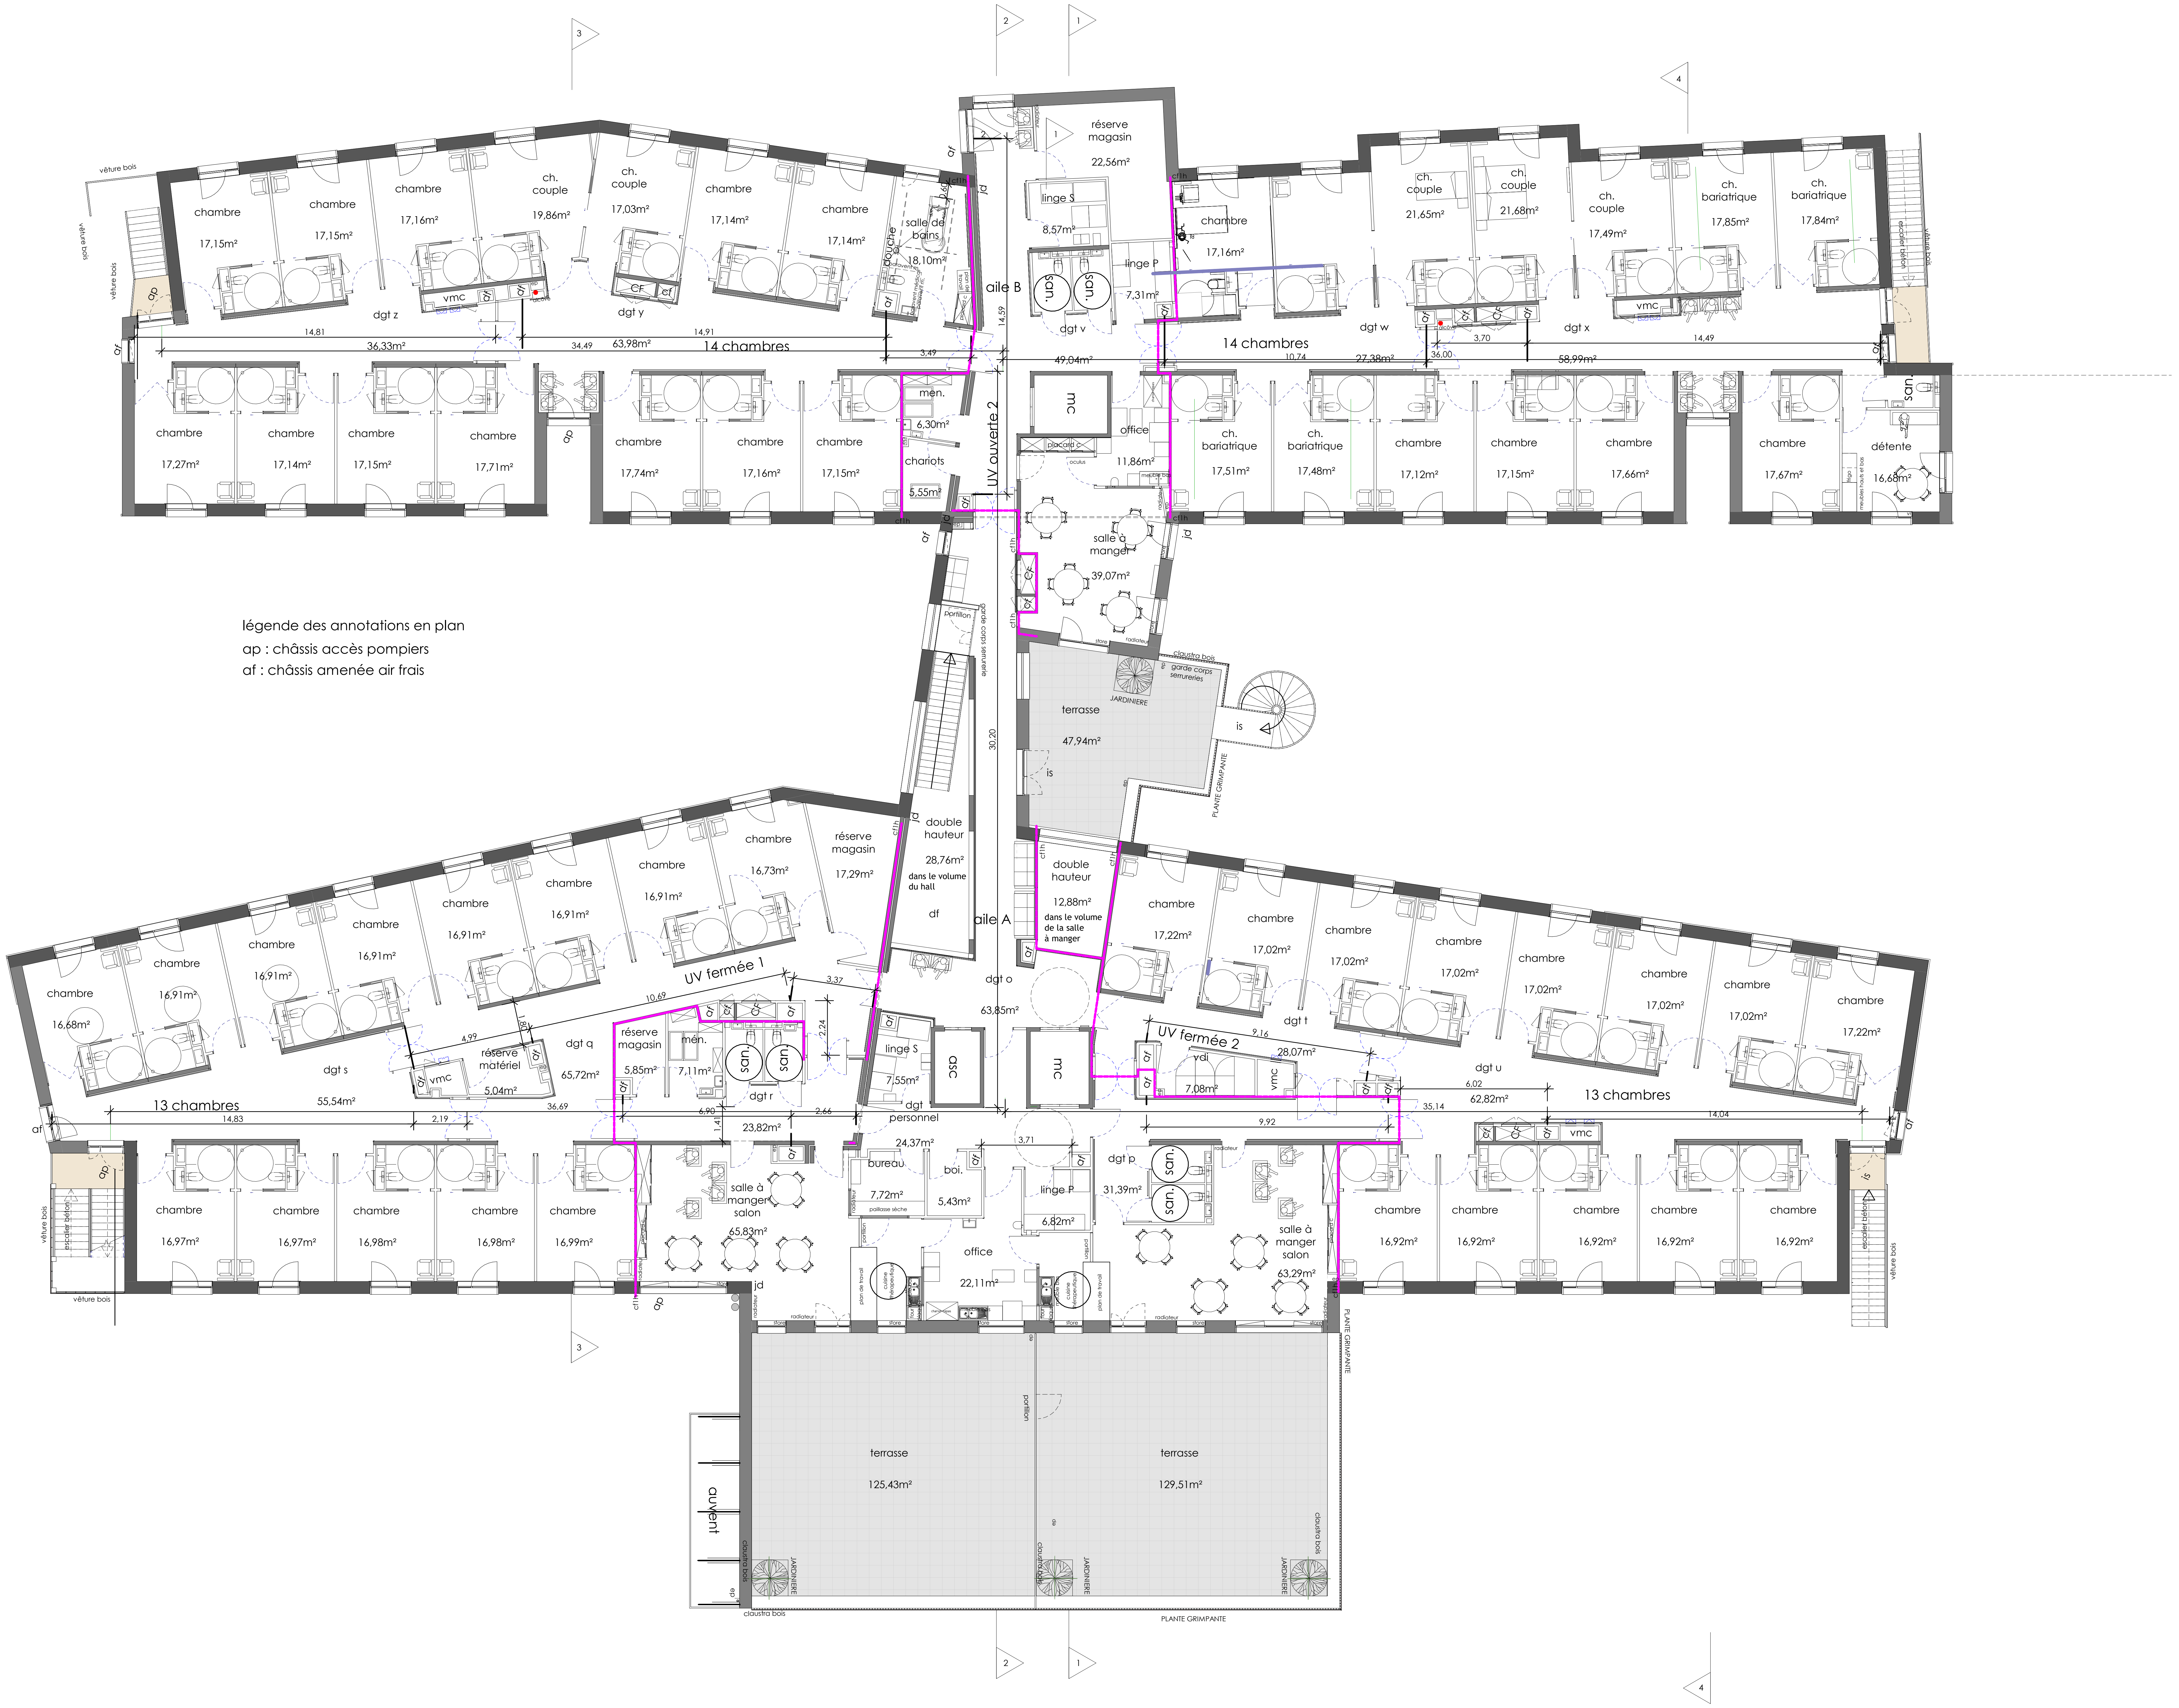

légende des annotations en plan
ap : châssis accès pompiers
af : châssis amenée air frais

Affaire n° : **19.05**

Projet : **EHPAD DE 81 LITS**
170 route de Lille, La Bassée

Maître d'ouvrage : GHT de l'Artois
CH LENS BAT A1 99 rte de La Bassée SP8 62307 Lens Cedex
tél : 03 21 69 16 37

AMO : MCI
120, rue Esquermes 59000 Lille
tél : 03 20 05 10 80

AMO : ASCOH
10, zac carrière dorée 59310 Orchies
tél : 07 69 47 80 12

Architectes PAINDAVOINE PARMENTIER
101 rue Louis Constant - 59650 Villeneuve d'Ascq
tél : 03 20 05 22 15

Architectes AVANT PROPOS
51, BVD de Belfort - 59042 Lille cedex
tél : 03 20 62 10 00

Paysagistes KVDS
340, av de la Marne - Parc Europe - Bat 11 - 59700 Marcq en Baroeul
tél : 03 20 89 39 80

BET PROJEX / PROBIM
30, place S. Allende - 59650 - Villeneuve d'Ascq
tél : 03 20 47 03 01

BET EGIS
165, av de la Marne - CS 32005 59702 Marcq-en-Baroeul Cedex
tél : 03 20 28 31 38

BET HQE DIAGOBAT
30, place S. Allende - 59650 - Villeneuve d'Ascq
tél : 03 20 47 23 20

Codification :

DCE	PPA	ARC		N1	TZ	AR02	0
PHASE	EMETTEUR	LOT	TYPE	NIVEAU	ZONE	NUMERO	INDICE

Nom du document : **PLAN DU R+1**
Echelle : 1/100
Modifications :

0	première diffusion	06/22
N°	Description	Date

20/06/2022 14:39:39