




23 VOLUME EST 2 FACE NORD
Ech : 1 : 50

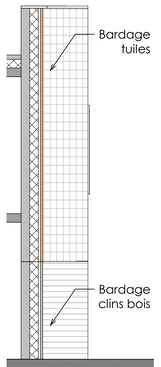


24 VOLUME EST 2 FACE SUD
Ech : 1 : 50

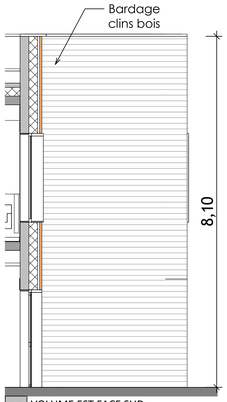


22 VOLUME EST FACE SUD
Ech : 1 : 50

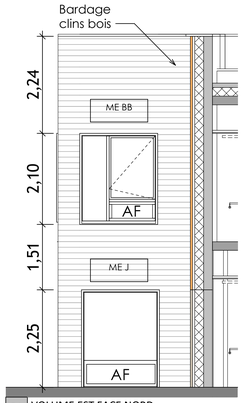


21 VOLUME EST FACE NORD
Ech : 1 : 50

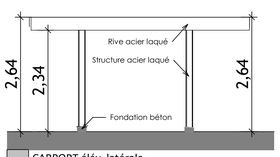


5 CARPORT élév. latérale
Ech : 1 : 50

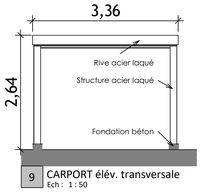


9 CARPORT élév. transversale
Ech : 1 : 50

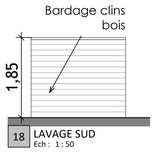


18 LAVAGE SUD
Ech : 1 : 50

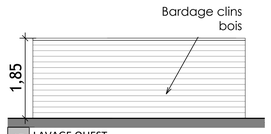

17 LAVAGE OUEST
Ech : 1 : 50

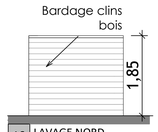


16 LAVAGE NORD
Ech : 1 : 50

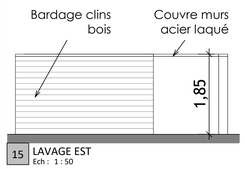


15 LAVAGE EST
Ech : 1 : 50




1 ELEVATION EST AILE B PC
Ech : 1 : 200

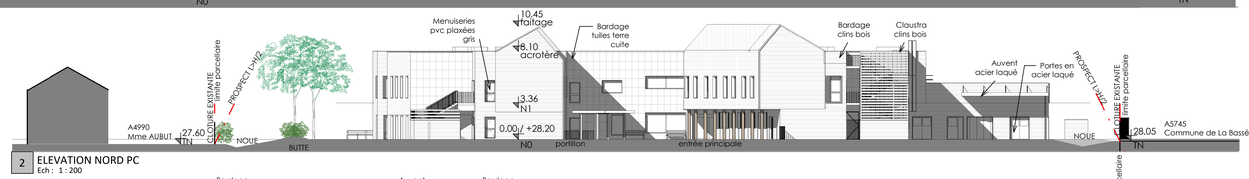


2 ELEVATION NORD PC
Ech : 1 : 200

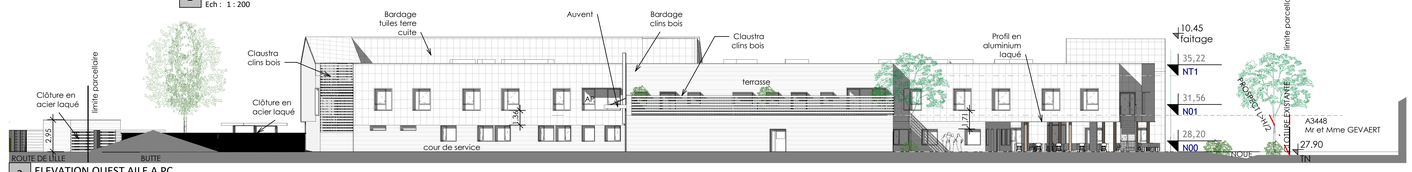


3 ELEVATION OUEST AILE A PC
Ech : 1 : 200

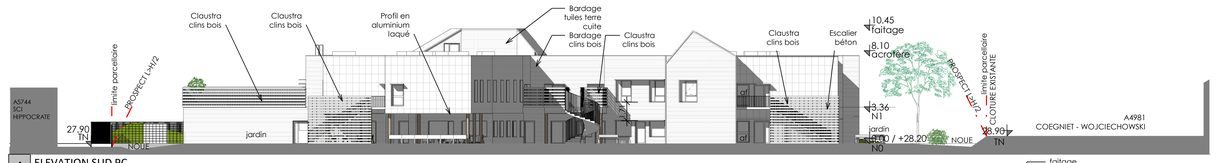


4 ELEVATION SUD PC
Ech : 1 : 200

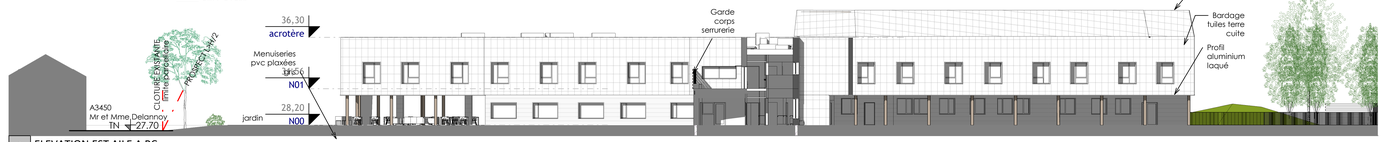


6 ELEVATION EST AILE A PC
Ech : 1 : 200

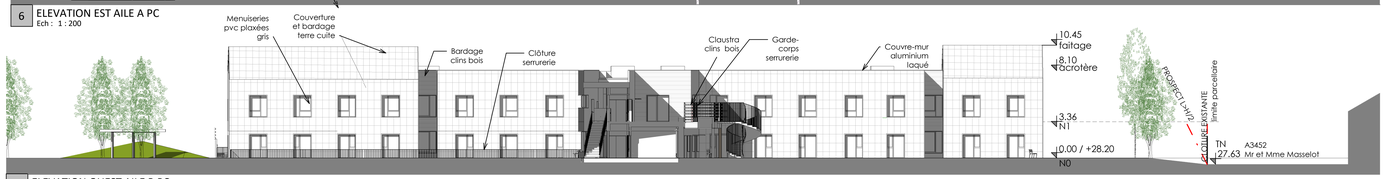


7 ELEVATION OUEST AILE B PC
Ech : 1 : 200

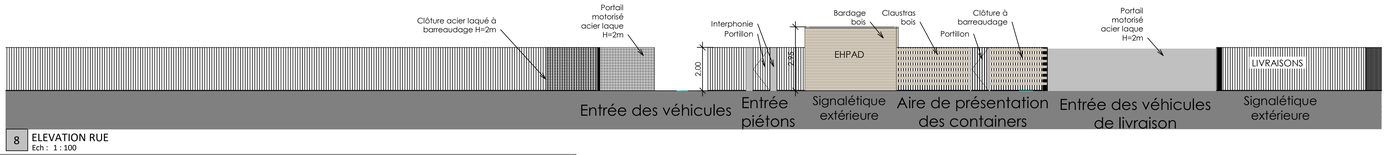


8 ELEVATION RUE
Ech : 1 : 100

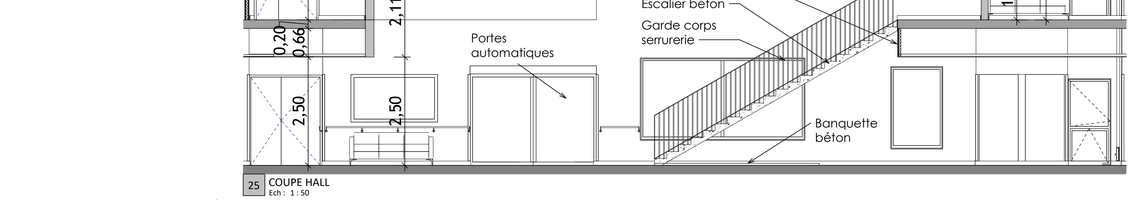


25 COUPE HALL
Ech : 1 : 50

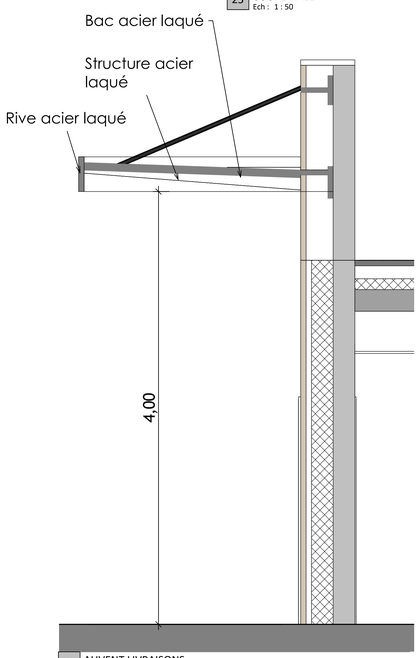


26 AUVENT LIVRAISONS
Ech : 1 : 20

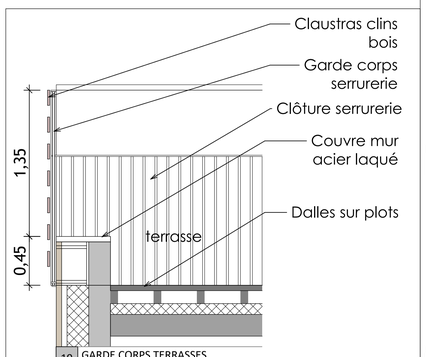

19 GARDE CORPS TERRASSES
Ech : 1 : 20

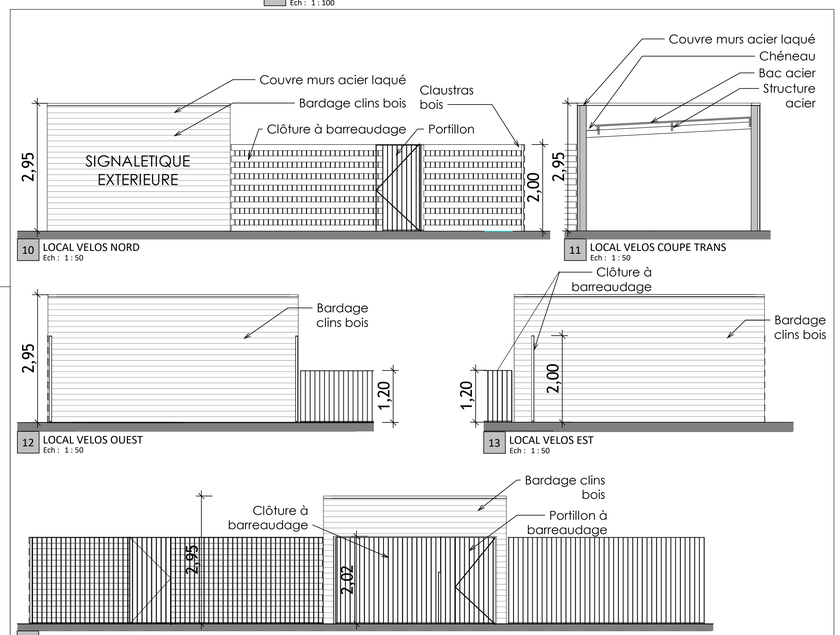

10 LOCAL VELOS NORD
Ech : 1 : 50
11 LOCAL VELOS COUPE TRANS
Ech : 1 : 50
12 LOCAL VELOS OUEST
Ech : 1 : 50
13 LOCAL VELOS EST
Ech : 1 : 50
14 LOCAL VELOS SUD
Ech : 1 : 50

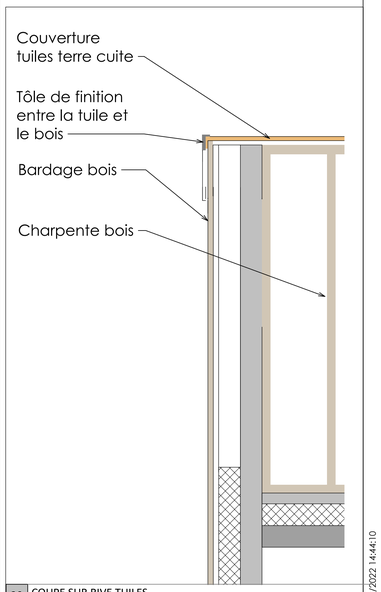

20 COUPE SUR RIVE TUILES
Ech : 1 : 20

Affaire n° : **19.05**

Projet : **EHPAD DE 81 LITS**
170 route de Lille, La Bassée

Maître d'ouvrage : GHT de l'Artois
CH EDG BAT A1 99 rte de La Bassée SPB 62307 Lens Cedex
tél : 03 21 69 16 37

AMO : MCI
120, rue Etaquermes 59000 Lille
tél : 03 20 05 10 80

AMO : ASCOH
10, zac carrière dorée 59310 Orchies
tél : 07 69 47 80 12

Architectes : PAINDAVOINE PARMENTIER
101 rue Louis Constant - 59650 Villeneuve d'Ascq
tél : 03 20 05 22 15

Architectes : AVANT PROPOS
51, BVD de Belfort - 59042 Lille cedex
tél : 03 20 62 10 00

Paysagistes : KVDS
340, av de la Marne - Parc Europe - Bat 11 - 59700 Marcq en Baroeul
tél : 03 20 89 39 80

BET : PROJEX / PROBIM
30, place S. Allende - 59650 - Villeneuve d'Ascq
tél : 03 20 47 03 01

BET : EGIS
165, av de la Marne - CS 32005 59702 Marcq-en-Baroeul Cedex
tél : 03 20 28 31 38

BET HQE : DIAGOBAT
30, place S. Allende - 59650 - Villeneuve d'Ascq
tél : 03 20 47 23 20

Codification :

DCE	PPA					AR11	0
PHASE	EMETTEUR	LOT	TYPE	NIVEAU	ZONE	NUMERO	INDICE

Nom du document : **FACADES COUPES DETAILS**

Echelle : 1/200

Modifications :

N°	Description	Date
0	première diffusion	06/22

20/06/2022 14:44:10