




4 Coupe 1 transversale sam
Ech : 1 : 50

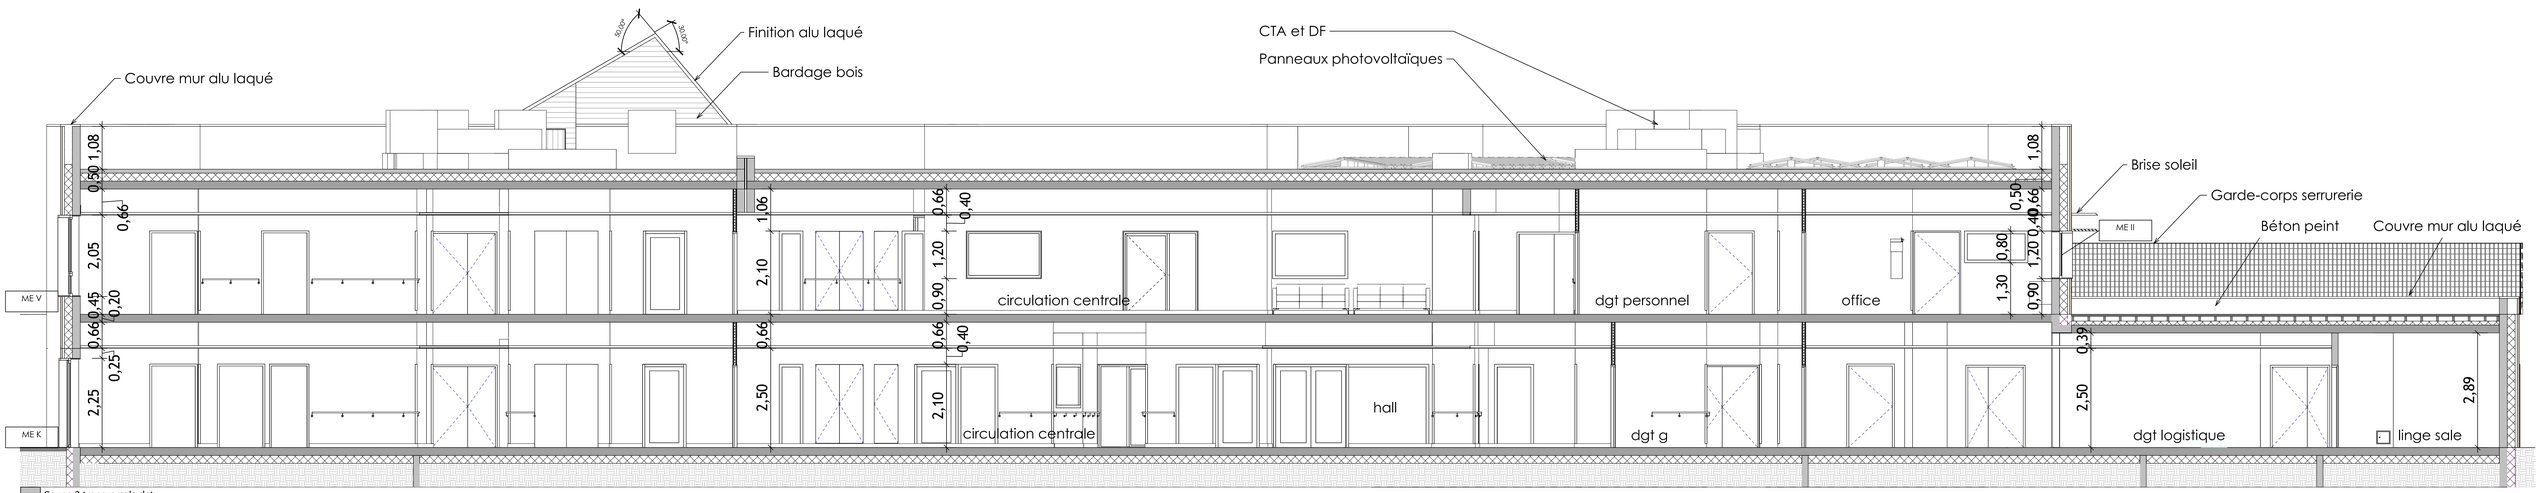


1 Coupe 2 transversale dgt
Ech : 1 : 50

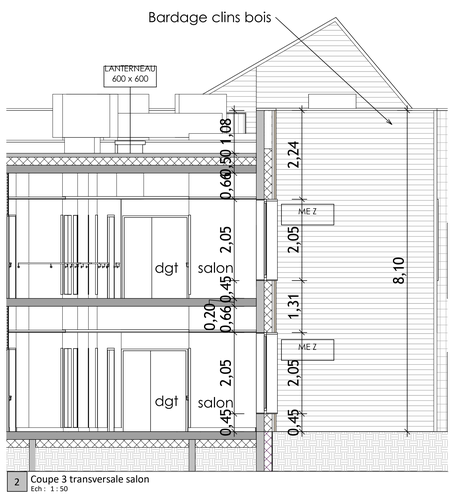

2 Coupe 3 transversale salon
Ech : 1 : 50

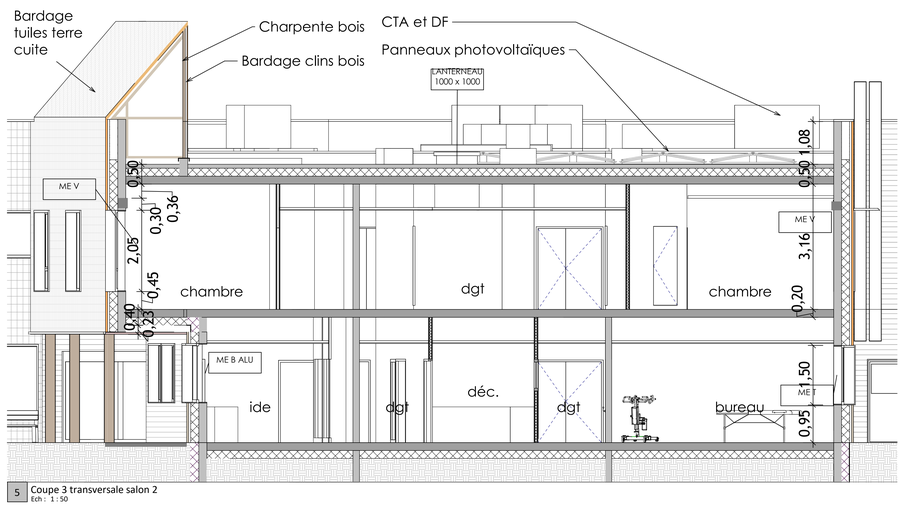

5 Coupe 3 transversale salon 2
Ech : 1 : 50

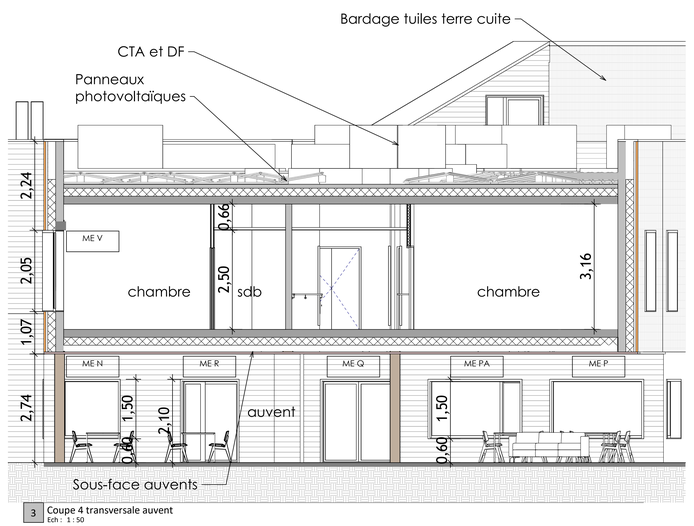

3 Coupe 4 transversale auvent
Ech : 1 : 50

Affaire n° : **19.05**

Projet : **EHPAD DE 81 LITS**
170 route de Lille, La Bassée

Maître d'ouvrage : GHT de l'Artois
CH LENS BAT A1 99 rte de La Bassée SP8 62307 Lens Cedex
tél : 03 21 69 16 37

AMO : MCI
125, rue Esquermes 59000 Lille
tél : 03 20 05 10 80

AMO : ASCOH
10, ass. carrière dorée 59310 Orchies
tél : 07 69 47 80 12

Architectes PAINDAVOINE PARMENTIER
101 rue Louis Constant - 59650 Villeneuve d'Ascq
tél : 03 20 05 22 15

Architectes AVANT PROPOS
51, BVD de Belfort - 59042 Lille cedex
tél : 03 20 62 10 00

Paysagistes KVDS
340, av. de la Marne - Parc Europe - Bat 11 - 59700 Marcq en Baroeul
tél : 03 20 89 39 80

BET PROJEX / PROBIM
30, place S. Allende - 59650 - Villeneuve d'Ascq
tél : 03 20 47 03 01

BET EGIS
165, av. de la Marne - CS 33005 59702 Marcq-en-Baroeul Cedex
tél : 03 20 28 31 38

BET HQE DIAGOBAT
30, place S. Allende - 59650 - Villeneuve d'Ascq
tél : 03 20 47 23 20

Codification :	DCE	PPA					AR15	0
	PHASE	EMETTEUR	LOT	TYPE	NIVEAU	ZONE	NUMERO	INDICE

Nom du document : **COUPES ELEVATIONS**
Echelle :
Modifications :

N°	Description	Date
0	première diffusion	06/22

20/06/2022 14:51:08