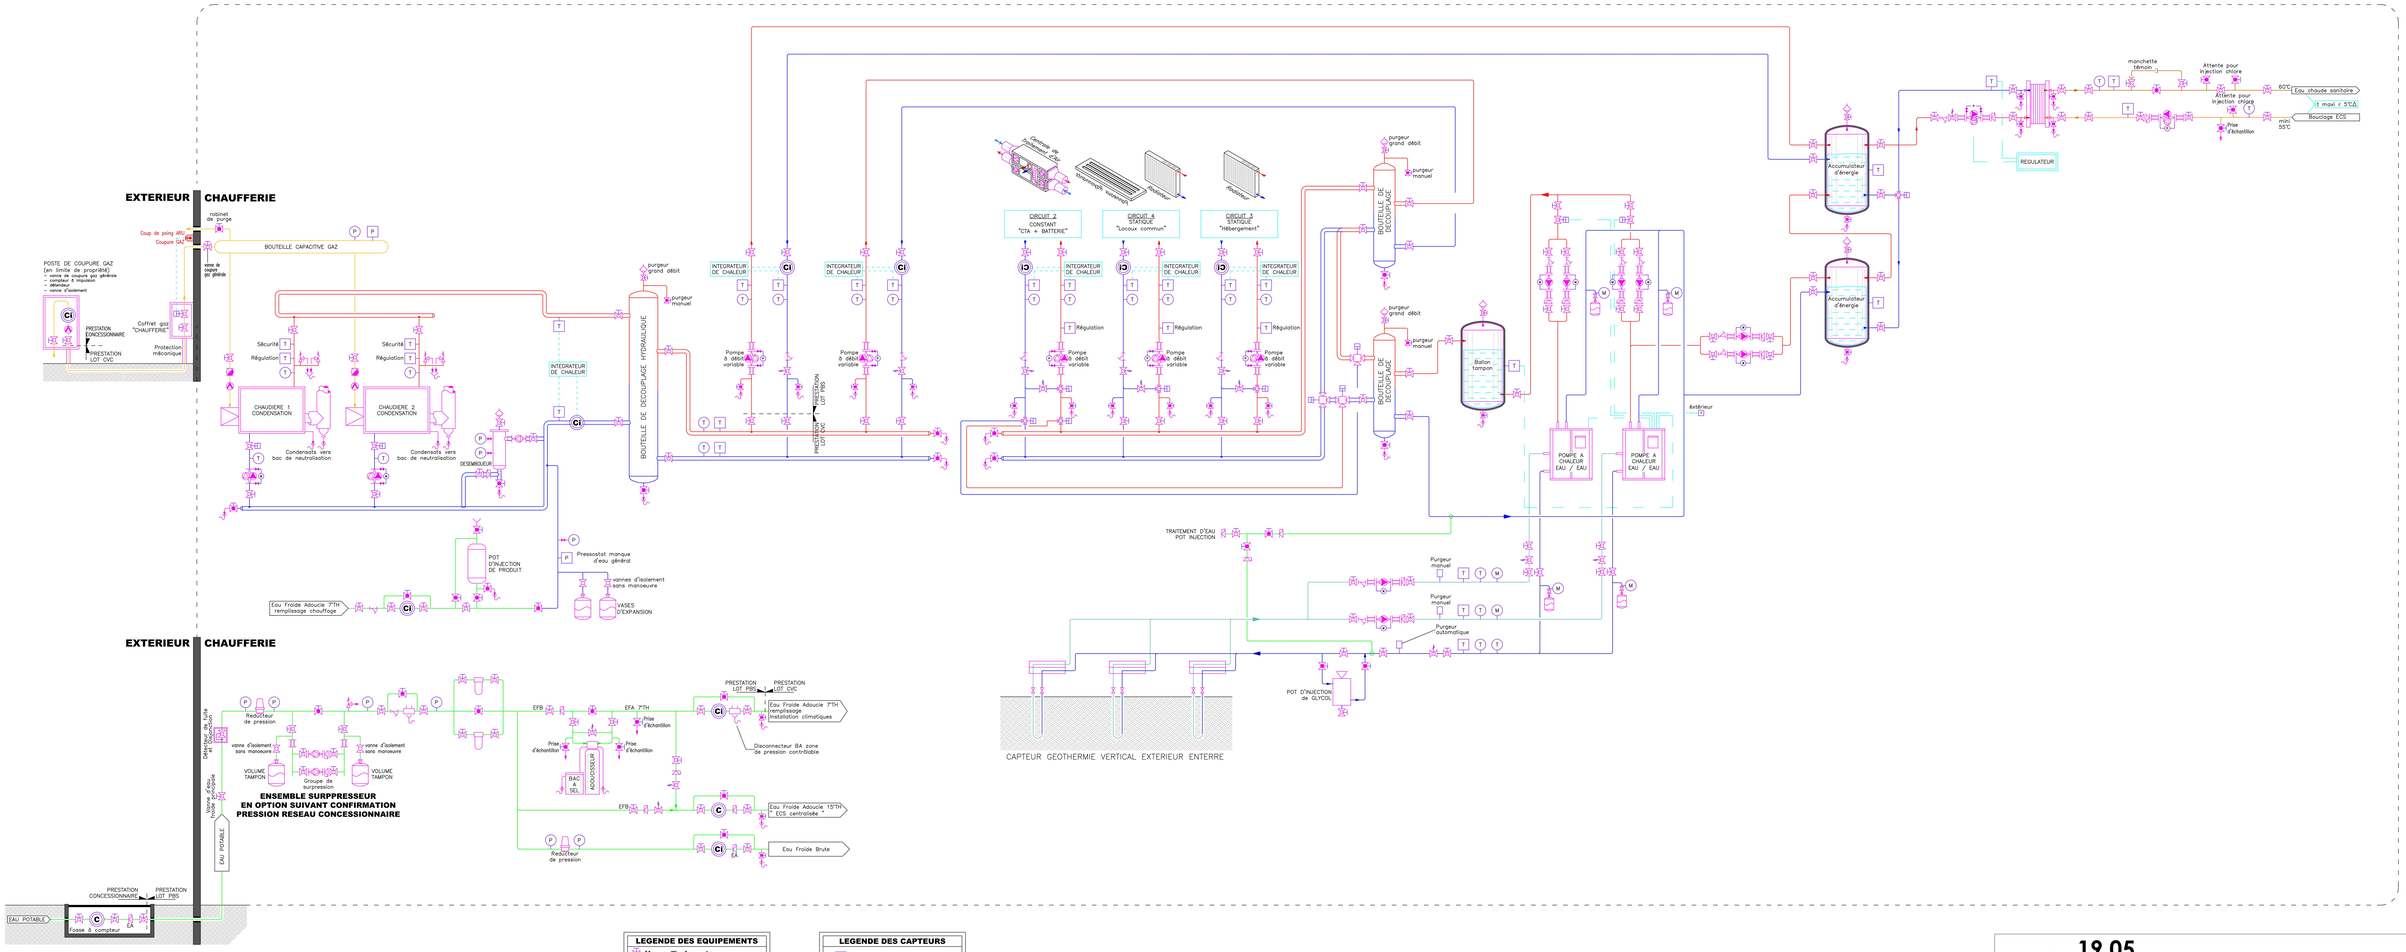


LEGENDE DES EQUIPEMENTS
Vanne d'isolement (normalement ouverte)
Vanne d'isolement (normalement fermée)
Vanne de réglage
Vanne 2 voies motorisée
Vanne 3 voies motorisée
Organe multi - régulation
Pompe double hydraulique
Pompe simple hydraulique
Manchon antivibratile
Clapet anti-retour
Disconnecteur controlable type BA
Soupape de sécurité
Purgeur
Anti-bélier
Filtre à tamis
Filtre à cartouche
Filtre gaz
Détendeur gaz
Evacuation en puisard ou caniveau
Détecteur de fuite et Disjonction
Réducteur de pression
Compteur — Compteur impulsion

LEGENDE DES CAPTEURS	
Transmetteur / Indicateur	
T	Température
P	Pression
D	Débit
H	Hygrométrie

LEGENDE DES RESEAUX
Canalisation Gaz
Chauffage - Aller
Chauffage - Retour
Eau Glacée - Aller
Eau Glacée - Retour
Eau Froide Sanitaire
Eau Chaude Sanitaire
Bouclage d'ECS

Affaire n° : **19.05**

Projet : **EHPAD DE 81 LITS**
170 route de Lille, La Bassée

Maître d'ouvrage : GHT de l'Artois
CH LENS BAT A1 99 rte de La Bassée SPB 62307 Lens Cedex
tél : 03 21 69 14 37

AMO : MCI
120, rue Esquermes 59000 Lille
tél : 03 20 05 10 80

AMO : ASCOH
10, ass. cantine dorée 59310 Orchies
tél : 07 69 47 80 12

Architectes PAINDAVOINE PARMENTIER
6, rue du moulin de Lezennes - 59650 Villeneuve d'Ascq
tél : 03 20 05 22 15

Architectes AVANT PROPOS
51, BVD de Belfort - 59042 Lille cedex
tél : 03 20 62 10 00

Paysagistes KVDS
340, av. de la Marne - Parc Europe - Bat 11 - 59700 Marcq en Baroeul
tél : 03 20 89 39 80

BET PROJEX / PROBIM
30, place S. Allende - 59650 - Villeneuve d'Ascq
tél : 03 20 47 03 01

BET EGIS
40, av. de la Marne - CS 50071 59442 Wasquehal Cedex
tél : 03 20 28 31 38

BET HQE DIAGOBAT
30, place S. Allende - 59650 - Villeneuve d'Ascq
tél : 03 20 47 23 20

Codification :

DCE	PJX	CVC-PBS	SCH			CVC-S-1	
PHASE	EMETTEUR	LOT	TYPE	NIVEAU	ZONE	NUMERO	INDICE

Nom du document : CHAUFFAGE + ECS + EAU GLACEE
Echelle : SANS
Modifications :

N°	Description	Date

01/06/2022 15:09:16