
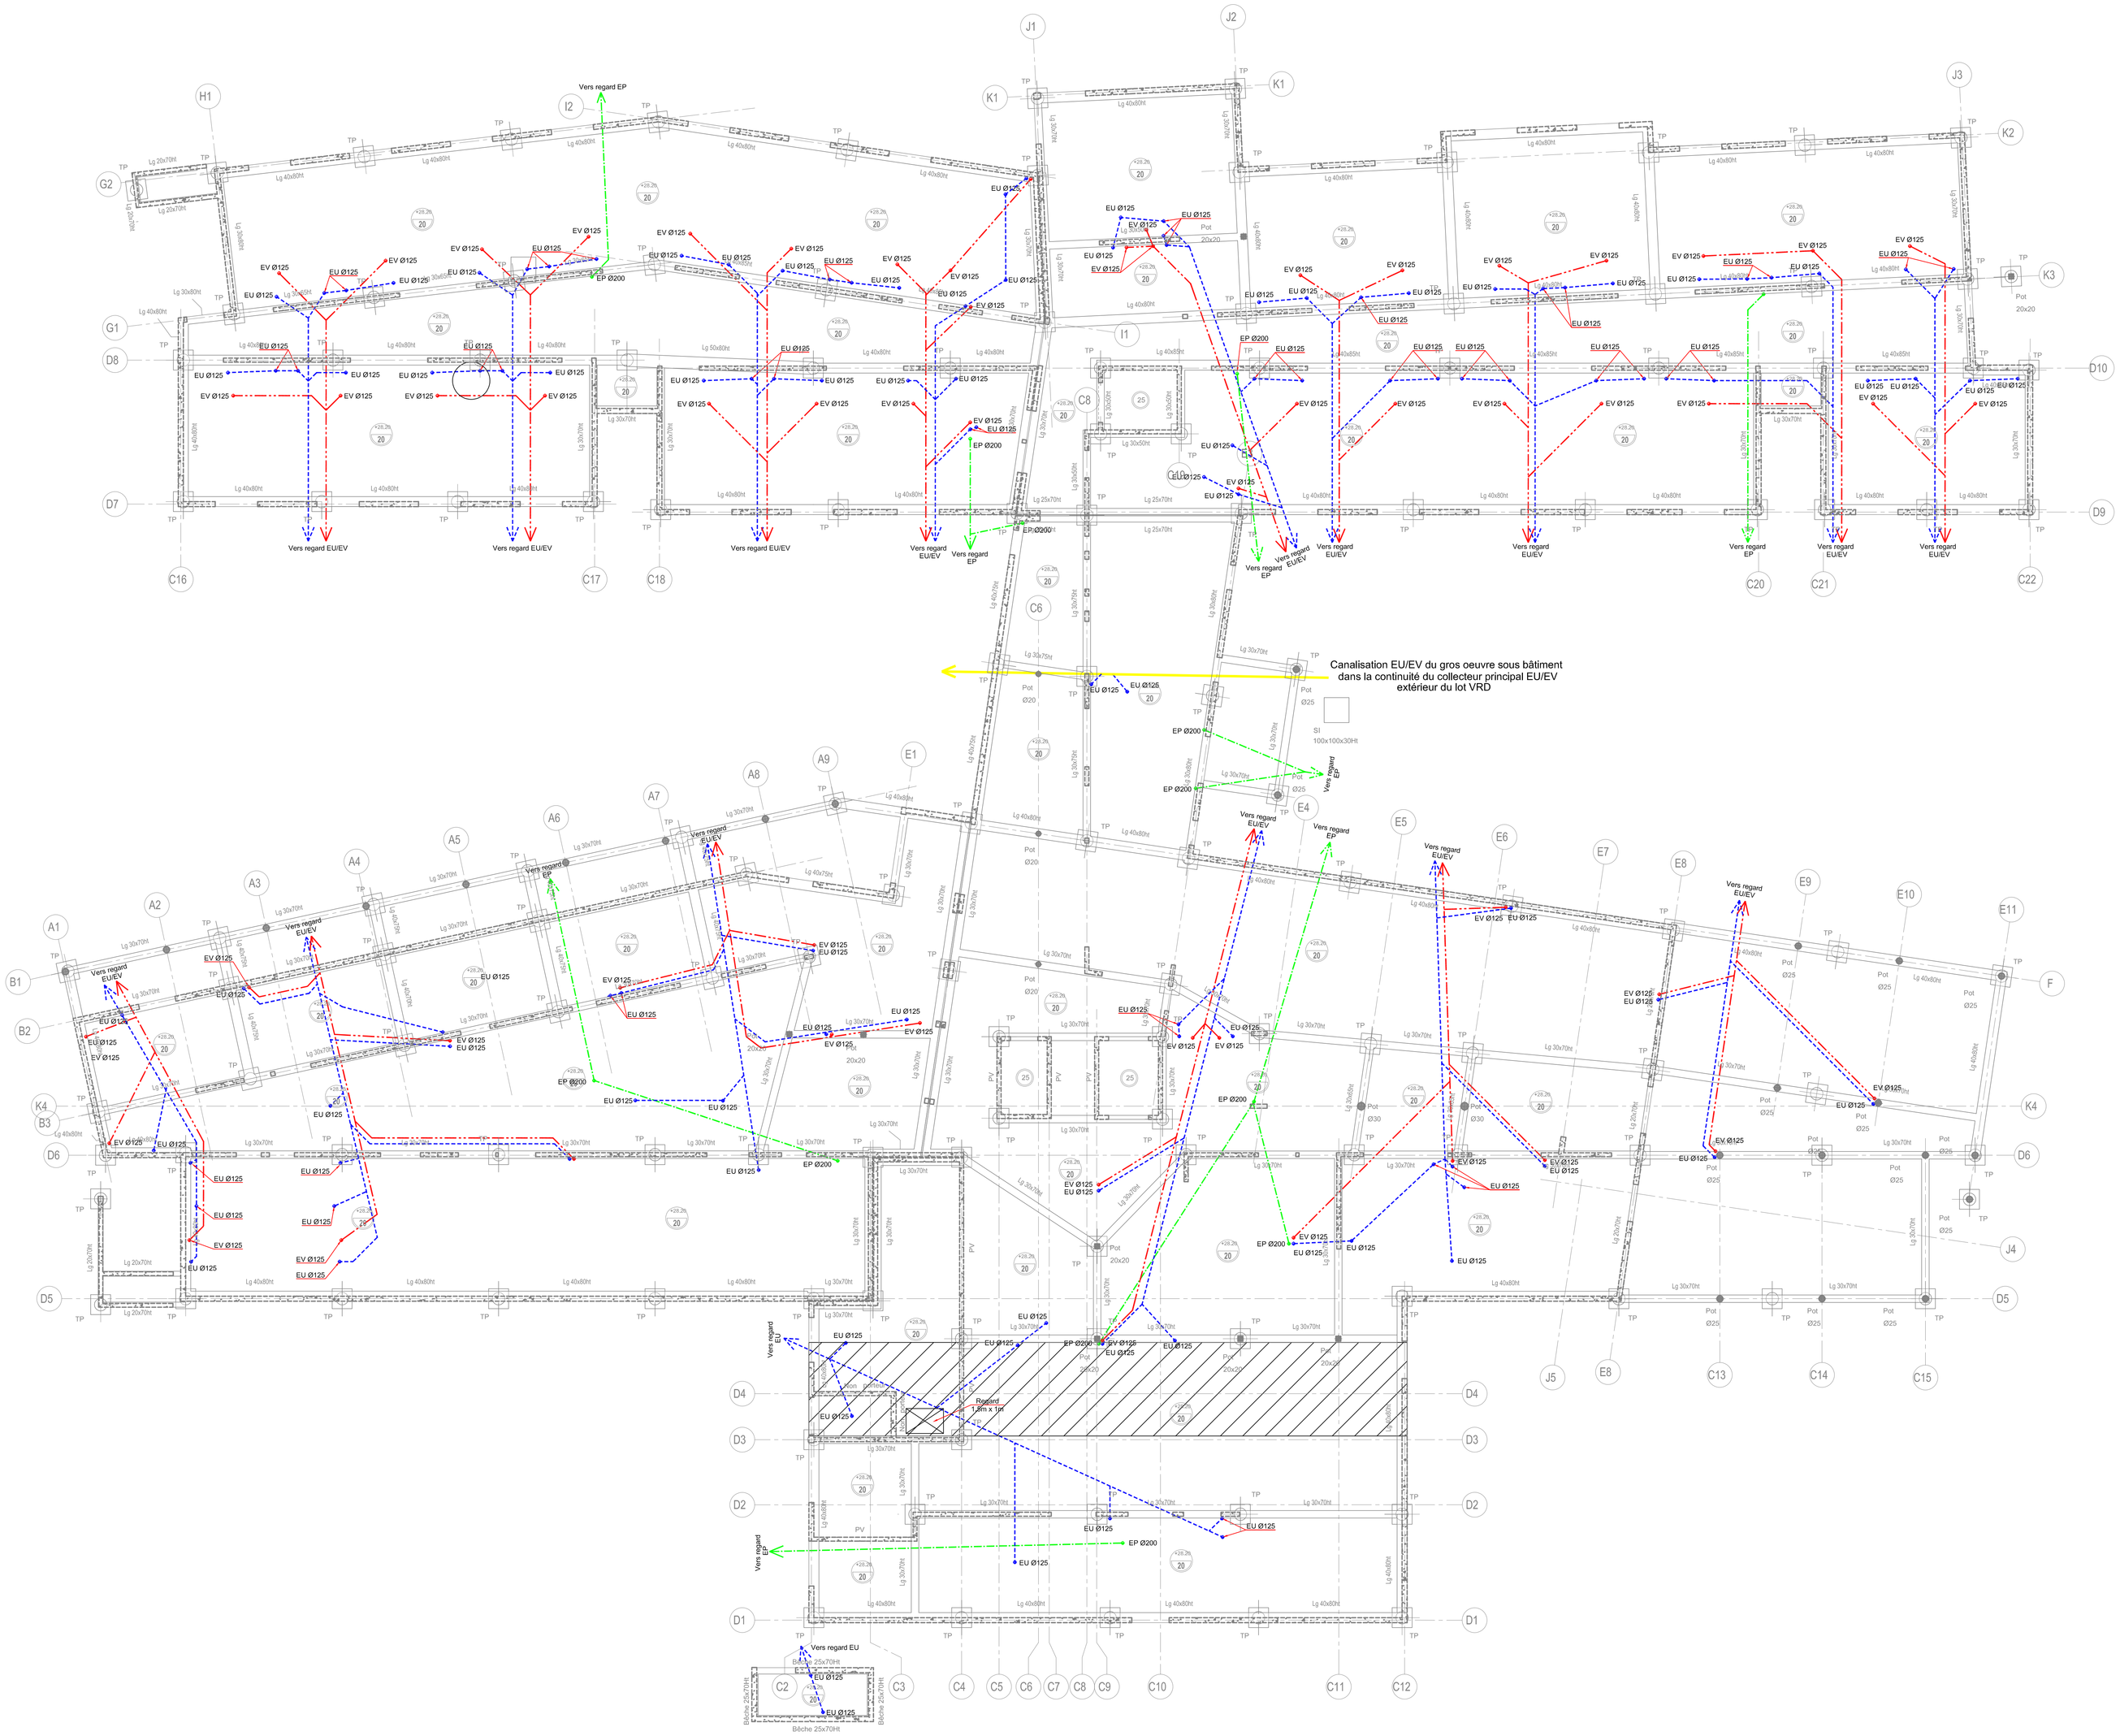


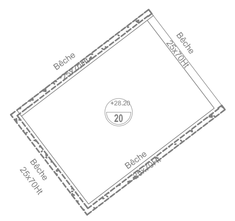

Légende

- EU
- EV
- EP
- Zone de passage de réseaux géothermie depuis sondes géothermiques enfuis entre -1m et -1.20m du niveau fini

NOTA :
Ce plan est un principe de structure et ne peut en aucun servir pour exécution.
Ce plan est établi à partir des plans architectes du 10/02/2022.
En cas de conflit entre les plans gros oeuvre et les plans architectes, les plans architectes sont prioritaires et l'entreprise devra adapter la structure conformément à ces derniers.

Niv 0.00 = +28.20NGF
Les niveaux indiqués sur les plans concernent la dalle brute.

CARACTERISTIQUES DES MATERIAUX UTILISES :
- BETON : C25/30 mini sauf indications contraires.
- ACIERS : HA Fe E500 - Dx Fe E235.

NORMES DE DIMENSIONNEMENTS
- Eurocode 0 : Bases de calculs de structure.
- Eurocode 1 : Actions sur les structures
- Eurocode 2 : Calcul des structures en béton armé.

Affaire n° : **19.05**

Projet : **EHPAD DE 81 LITS**
170 route de Lille, La Bassée

Maître d'ouvrage : GHT de l'Artois
CH LENS BAT A1 99 rte de La Bassée SP8 62307 Lens Cedex
Tél : 03 21 69 14 37

AMO : MCI
120, rue Eau-vermes 59000 Lille
Tél : 03 20 05 10 80

AMO : ASCOH
10, zac combles dorée 59310 Orchies
Tél : 07 69 47 80 12

Architectes : PAINDAVOINE PARMENTIER
6, rue du moulin de Lezennes • 59650 Villeneuve d'Ascq
Tél : 03 20 05 22 15

Architectes : AVANT PROPOS
51, BVD de Belfort - 59042 Lille cedex
Tél : 03 20 62 10 00

Paysagiste : KVDS
340, av de la Marne - Parc Europe • Bat 11 • 59700 Marcq en Baroeul
Tél : 03 20 89 39 80

BE : PROJEX / PROBIM
30, place S. Allende • 59650 - Villeneuve d'Ascq
Tél : 03 20 47 03 01

BET : EGIS
40, av de la Marne • CS 50071 59442 Wasquehal Cedex
Tél : 03 20 28 81 38

BET HQE : DIAGOBAT
30, place S. Allende - 59650 - Villeneuve d'Ascq
Tél : 03 20 47 23 20

Codification :	DCE	PJX					GO.04	0
	PHASE	ELEMENT	LOT	TYPE	SERVICE	ZONE	NUMERO	INDICE

Nom du document : **RESEAUX SOUS DALLE**

Echelle :

Modifications :

N°	Description	Date
0	Première diffusion	01/06/22

01/06/2022 10:28:00