

SYN-02 · EAU FROIDE ET PRODUCTION D'EAU CHAUDE SANITAIRE

Schéma de principe établi d'après le CCTP lot 12 (§4.5) et le schéma DCE CVC-S-1. Ne remplace pas le schéma d'exécution.

1 · ARRIVÉE ET TRAITEMENT DE L'EAU FROIDE

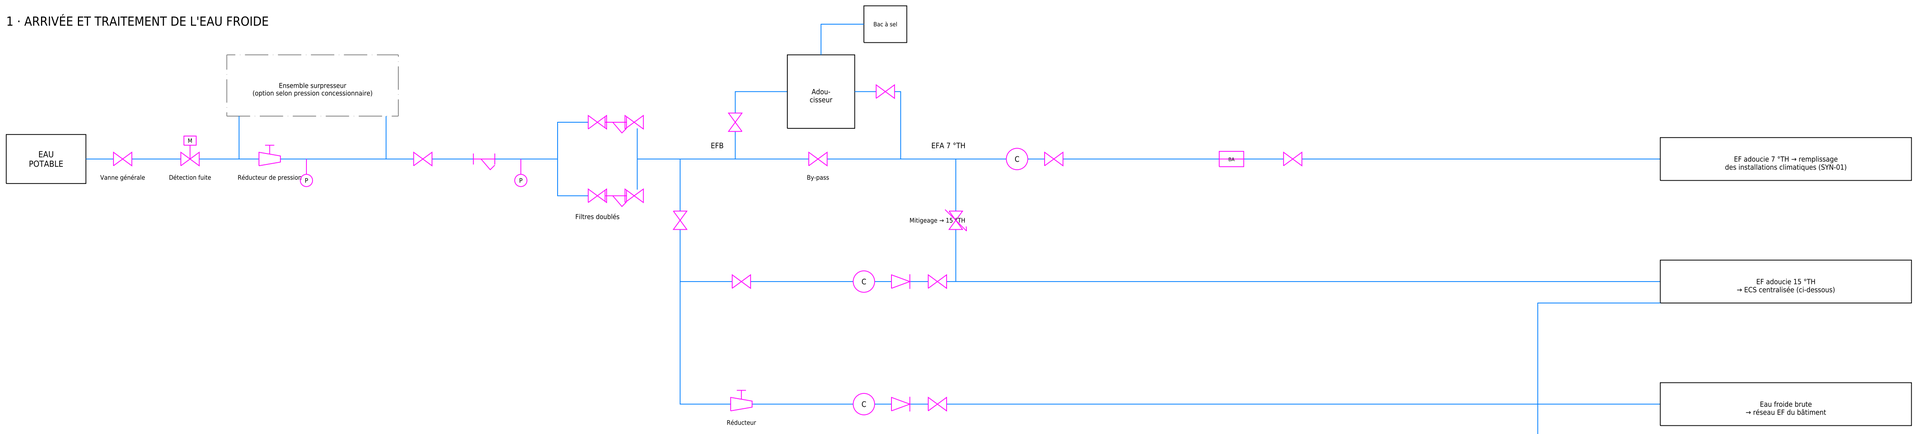

2 · PRODUCTION D'EAU CHAUDE SANITAIRE (CHAUFFERIE)

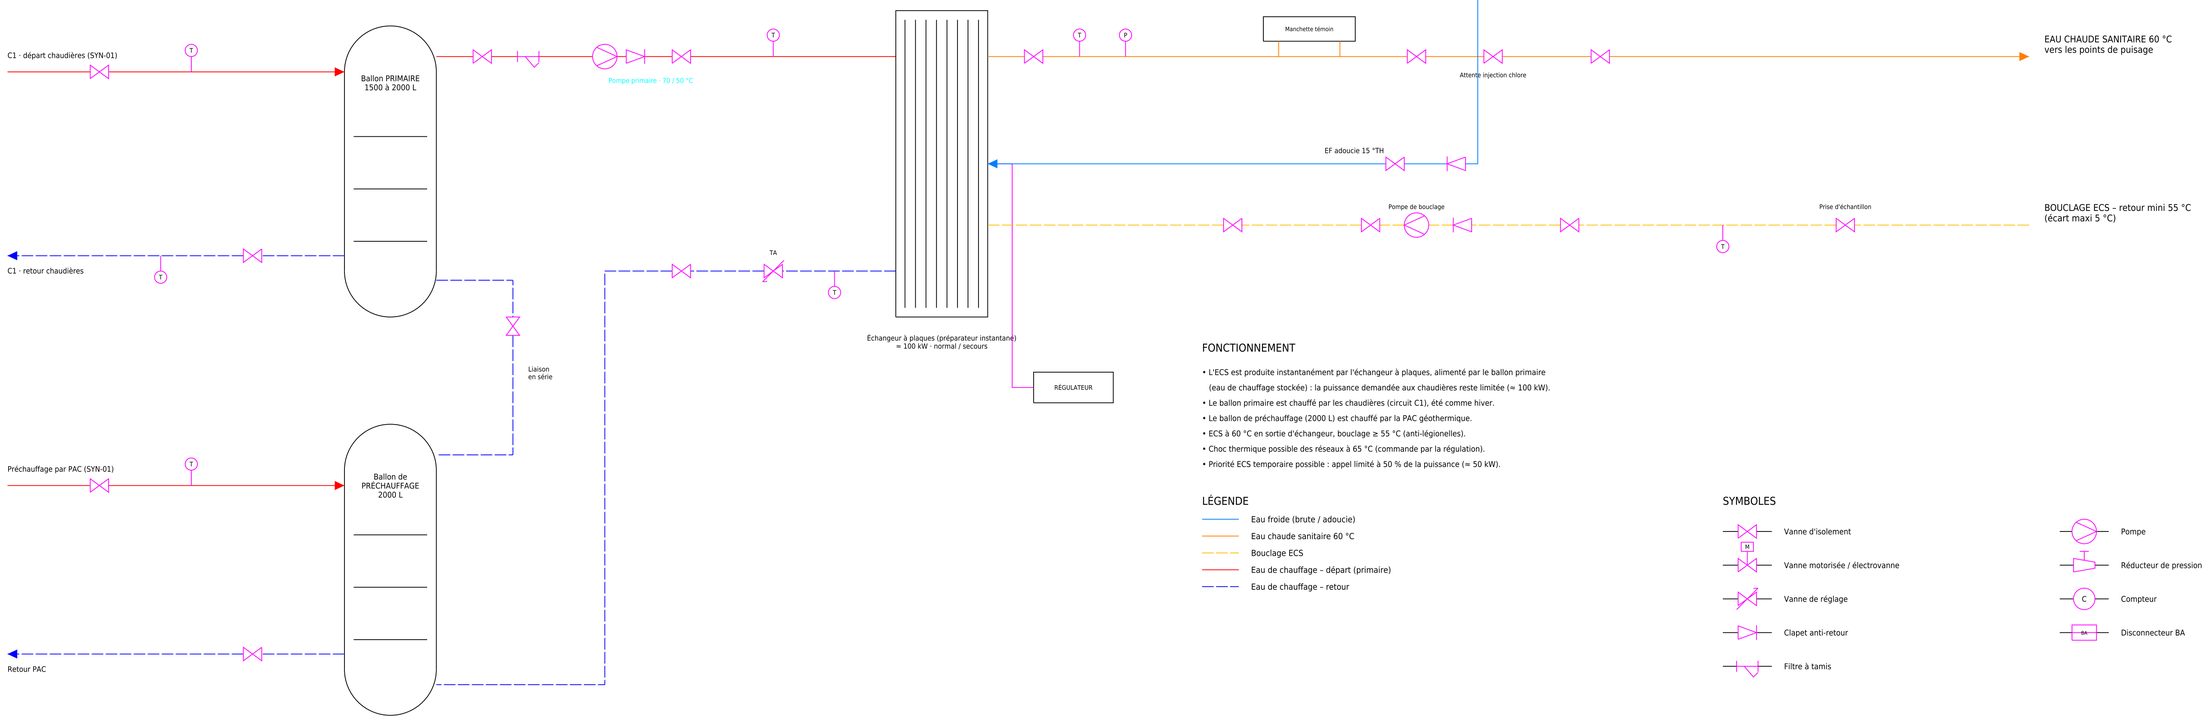

FONCTIONNEMENT

- L'ECS est produite instantanément par l'échangeur à plaques, alimenté par le ballon primaire (eau de chauffage stockée) : la puissance demandée aux chaudières reste limitée (≈ 100 kW).
- Le ballon primaire est chauffé par les chaudières (circuit C1), été comme hiver.
- Le ballon de préchauffage (2000 L) est chauffé par la PAC géothermique.
- ECS à 60 °C en sortie d'échangeur, bouclage ≥ 55 °C (anti-légionelles).
- Choc thermique possible des réseaux à 65 °C (commande par la régulation).
- Priorité ECS temporaire possible : appel limité à 50 % de la puissance (≈ 50 kW).

LÉGENDE

- Eau froide (brute / adoucie)
- Eau chaude sanitaire 60 °C
- Bouclage ECS
- Eau de chauffage – départ (primaire)
- Eau de chauffage – retour

SYMBOLES

- Vanne d'isolement
- Vanne motorisée / électrovanne
- Vanne de réglage
- Clapet anti-retour
- Filtre à tamis
- Pompe
- Réducteur de pression
- Compteur
- Disconnecteur BA

EHPAD de 81 lits – La Bassée (62)

Projet tutoré N°3 · Licence BIM-CVC · Lycée Raspail – CNAM

Synoptique eau froide et production ECS

Arrivée EF, adoucissement, stockage primaire, échangeur à plaques, ECS 60 °C et bouclage

N°	Indice	Date	Échelle	Lot
SYN-02	A	16/10/2026	Sans	12 CVC-PBS

Équipe : Allan · Mouhamed · Yann · Noah Source : CCTP lot 12 (juin 2022) + schéma DCE CVC-S-1